


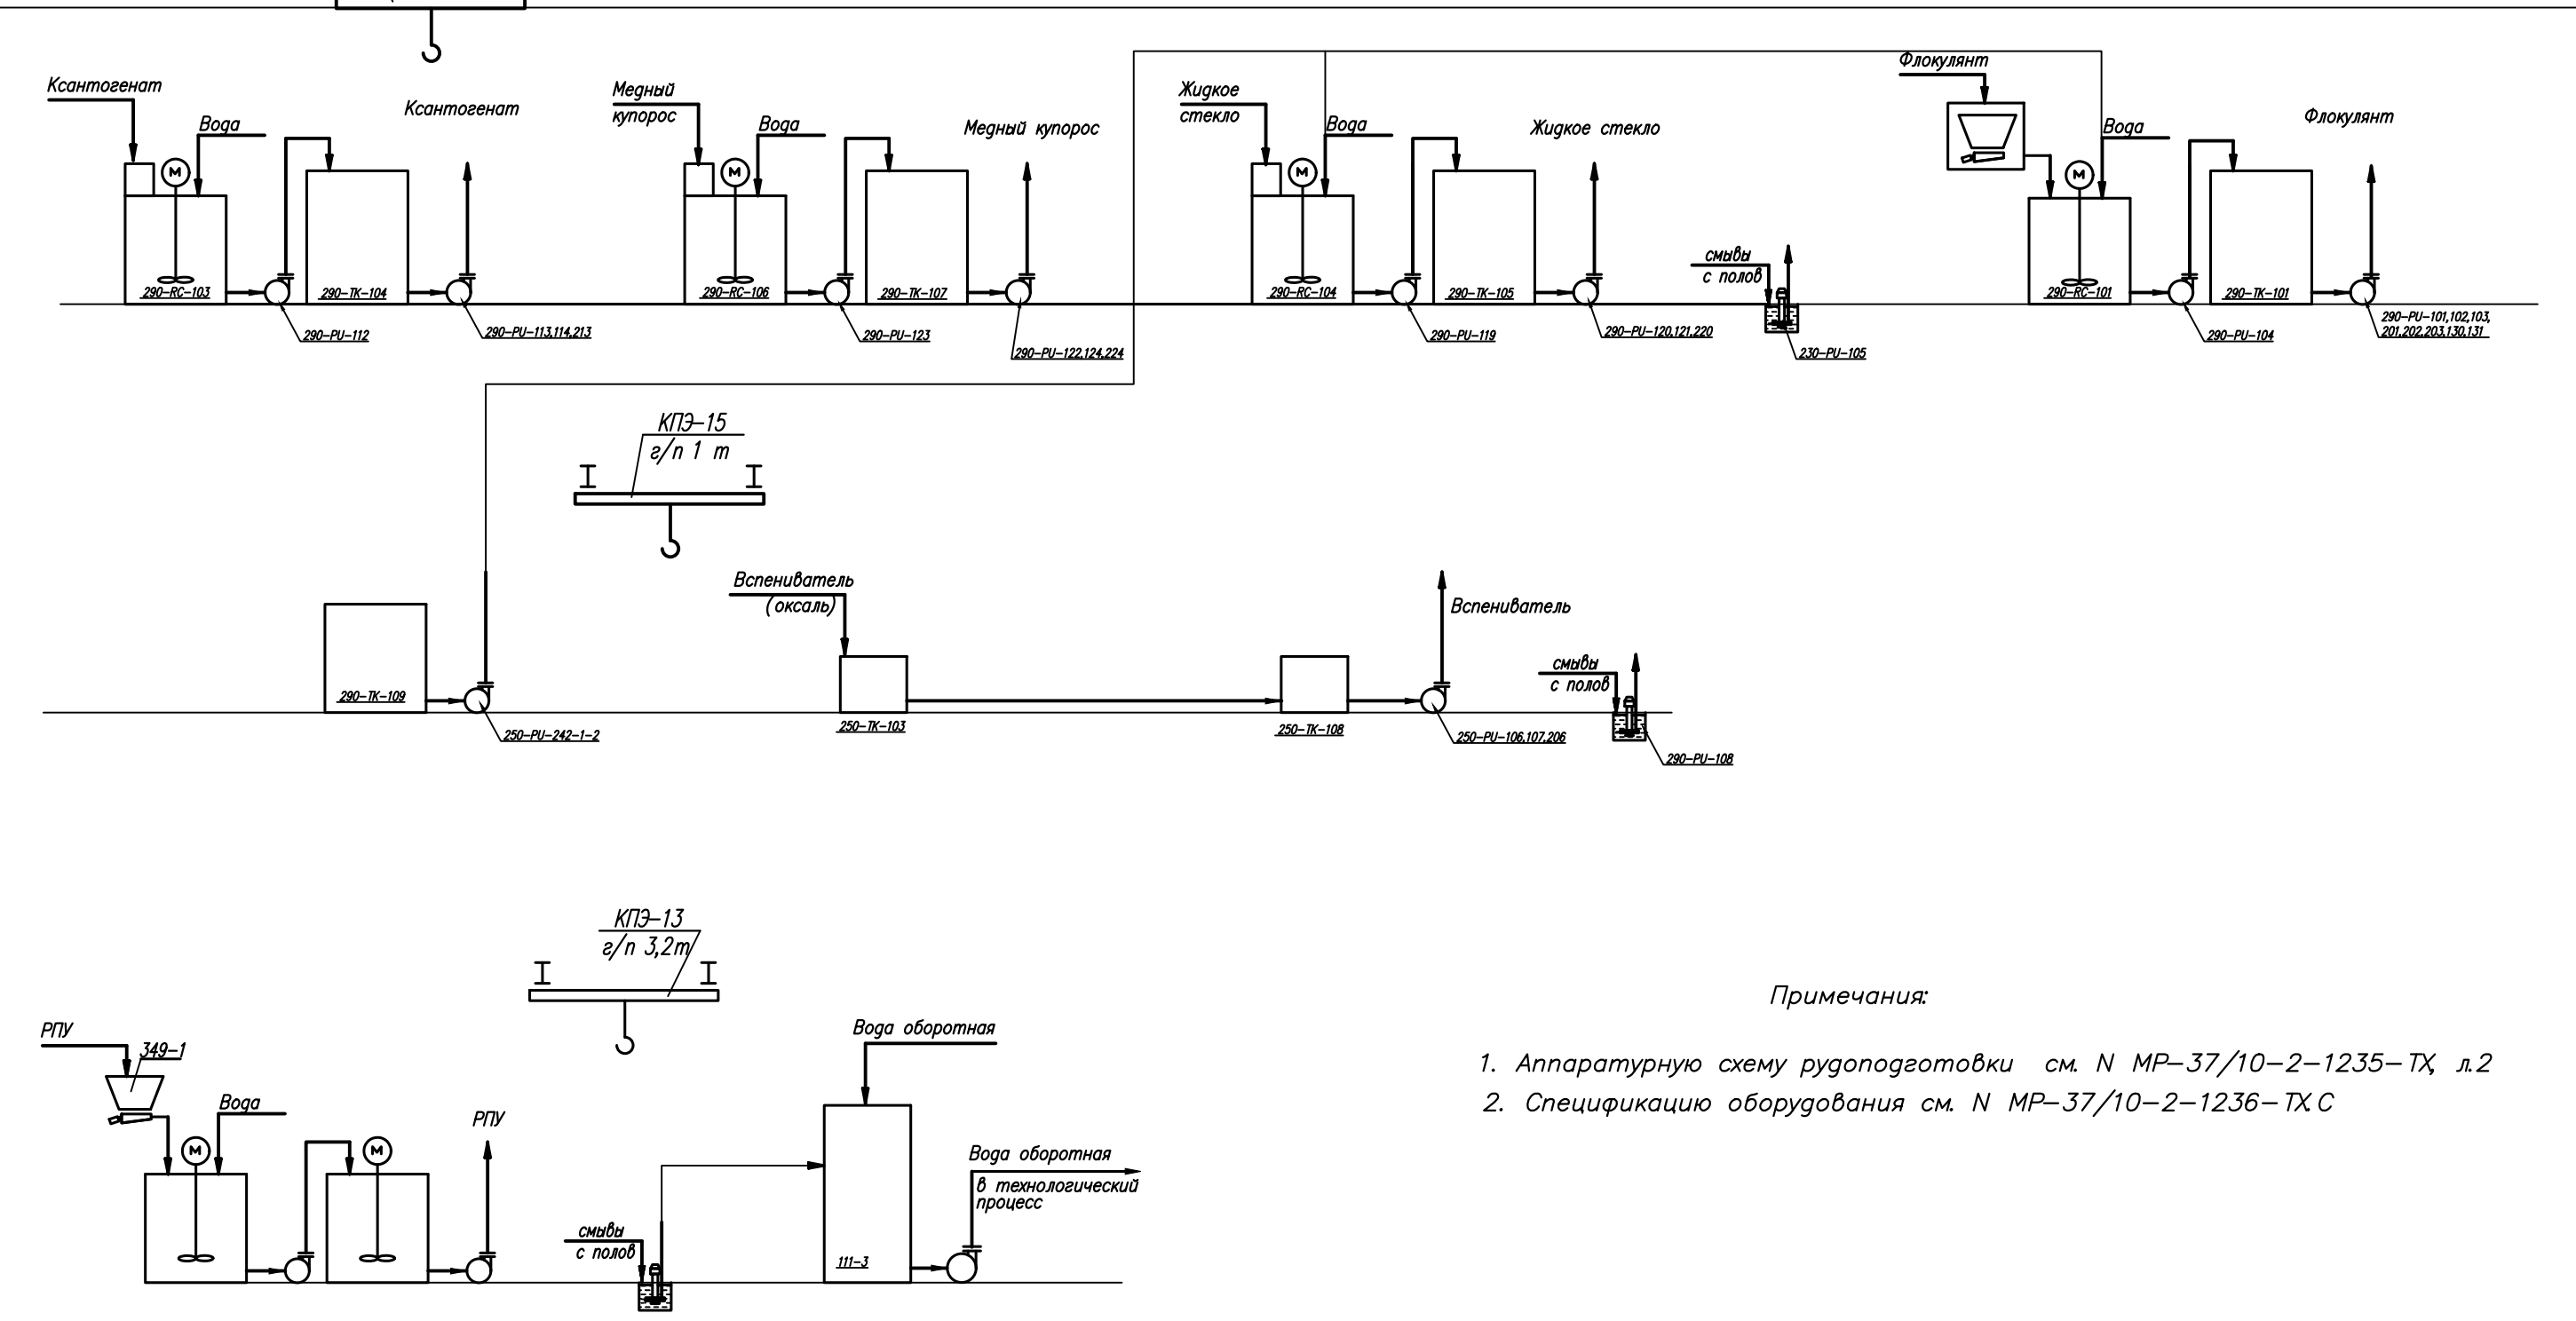

Примечания:

1. Аппаратурную схему рудоподготовки см. N МР-37/10-2-1235-ТХ л.2
2. Спецификацию оборудования см. N МР-37/10-2-1236-ТХ С

						МР-37/10-2-1235-ТХ
						Горнодобывающее предприятие на базе Маломырского золоторудного месторождения ООО "Маломырский рудник" <i>Первая очередь строительства и разработки месторождения</i>
Изм.	Код кн.	Лист	№ док.	Подп.	Дата	
Разработка	Сахарова					Статус Лист Листов
Пробирка	Зеленчев					P 3 6
H. контрл.	Панкова					
Нач. отг.	Зеленчев					
						Аппаратурная схема получения флотоконцентрата
						ЗАО "ПХМ Инжиниринг"